## План раскладки элементов мостового полотна

М 1:100

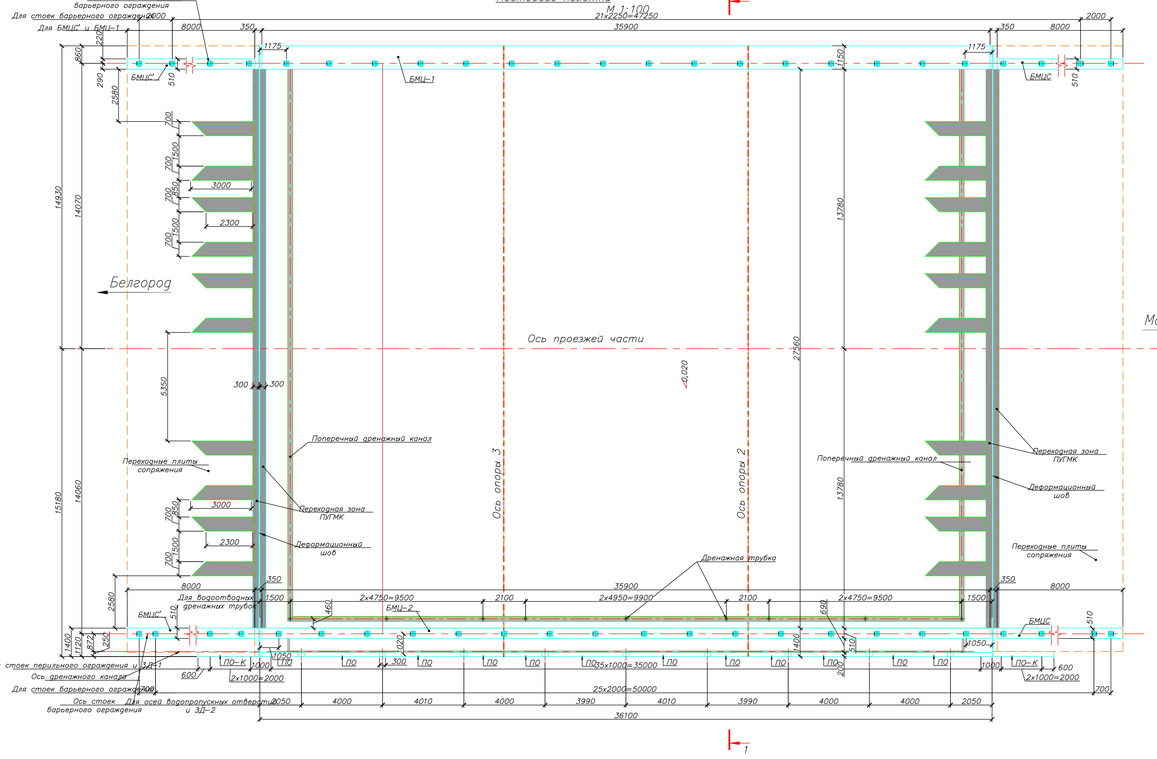


## Конструкция дренажного устройства ДУ.50

М 1:10

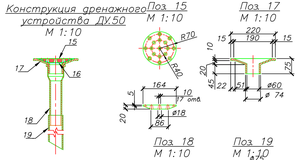


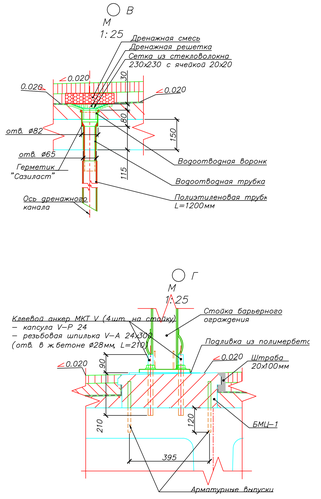


## Ведомость основных объемов работ по ремонту мостового полотна

| Поз. | Наименование | Ед. изм. | Кол–во |
|---|---|---|---|
| 1 | Фрезерование покрытия проезжей части на путепроводе | м²/м³ | 992,75/310,94 |
| 2 | Разборка оставшегося после фрезерования выравнивающего слоя до верха балок | м²/м³ | 992,75/109,93 |
| 3 | Разборка покрытия служебного прохода на путепроводе до верха балок | м²/м³ | 50,54/17,69 |
| 4 | Демонтаж металлического барьерного ограждения на путепроводе | п.м./т | 72,20/4,69 |
| 5 | Демонтаж железобетонных цоколей барьерного ограждения на путепроводе | м³ | 7,98 |
| 6 | Демонтаж перильного ограждения на путепроводе | пм./т | 36,20/1,26 |
| 7 | Демонтаж существующих деформационных швов | п.м. | 60,22 |
| 8 | Разборка части консоли плиты крайней балки на всю длину пролетного строения, на ширину 0,39 м | м³ | 2,11 |
| 9 | Устройство монолитных цоколей БМЦС под стойки барьерного ограждения на сопряжении ПГМК с консолью мост. | шт./м³ | 4/4,72 |
| 10 | Устройство монолитной части консоли УМК с цоколем под перильное ограждение В40 F300 (в солях) W12 | м³ | 3,97 |
| | Устройство закладных деталей ЗД–1 под стойки перильного ограждения | шт. | 42 |
| | Устройство закладных деталей ЗД–2 в местах примыкания плиты к бортовому брусу | шт. | 9 |
| 11 | Устройство бетонной подготовки бетона открылков крайних опор в местах установки закладных деталей под стойки перильного ограждения ЗД–1 | м³ | 1,65 |
| 12 | Устройство арматурных выпусков (с шагом 200мм) из плит крайних балок в монолитные цоколя БМЦ–1 и БМЦ–2: | | |
| | – арматура ø12 А–III, L=255мм | шт./кг | 360/81,52 |
| | – арматура ø12 А–III, L=330мм | шт./кг | 540/158,24 |
| | – клеевой состав на основе эпоксидной смолы | л | 13,30 |
| | эпоксидная смола "ЗД–20" | л | 2,70 |
| | отвердитель "ПЭПА" | | 900/108,00 |
| | Бурение отверстий в железобетоне ø16 мм, l=120мм | шт./п.м. | |
| 13 | Устройство монолитного цоколя БМЦ–1 под стойки барьерного ограждения В40 F300 (в солях) W12 | м³ | 3,27 |
| 14 | Устройство монолитного цоколя БМЦ–2 под стойки барьерного ограждения В40 F300 (в солях) W12 | м³ | 12,21 |
| 15 | Пластикатрба трубка ПЭ63 SDR11–32x3.0 по ГОСТ 18599–2001; L=270 мм | шт./кг | 9/0,63 |
| 16 | Устройство дренажных каналов 100Х50 мм в зоне служебного прохода с применением дренажной смеси по рецептуре "СОЮЗДОРНИИ" | п.м./м³ | 34,72/0,17 |
| 17 | Дренажная решетка РВ 160 20, чугун марки СЧ–20 по ГОСТ412–85 | шт./кг | 9/9,00 |
| 18 | Сетка из стеклоболокна 230х230 (ячейка 20х20) | м² | 1,00 |
| 19 | Дренажная воронка ВР 50 220 75, чугун марки СЧ–20 по ГОСТ412–85 | шт./кг | 9/40,50 |
| 20 | Дренажная трубка ЧК 50, чугун марки СЧ–20 по ГОСТ412–85; L=300 мм | шт./кг | 9/20,25 |
| 21 | Пластикатрба трубка ПЭ63 SDR11–75x6,8 по ГОСТ 18599–2001; L=1200 мм | шт./кг | 9/15,77 |
| 22 | Устройство дренажных каналов 240Х50 мм на проезжей части с применением дренажной смеси по рецептуре "СОЮЗДОРНИИ" | п.м./м³ | 87,30/1,05 |
| 23 | Устройство выравнивающего слоя на проезжей части, В30 F300 W6 | м²/м³ | 994,92/261,19 |
| 24 | Устройство гидроизоляции проезжей части "Техноэластмост С" – 5,5 | м² | 1009,00 |
| 25 | Устройство нижнего слоя покрытия проезжей части Литой асфальтобетон – 50 мм | м²/м³ | 994,92/49,75 |
| 26 | Устройство верхнего слоя покрытия проезжей части Литой асфальтобетон – 50 мм | м²/м³ | 994,92/49,75 |
| 27 | Устройство выравнивающего слоя служебного прохода, h=45мм, В30 F300 W6 | м²/м³ | 26,85/1,21 |
| 28 | Устройство гидроизоляции служебного прохода "Техноэластмост С" – 5,5 | м² | 31,00 |
| 29 | Устройство защитного слоя служебного прохода, h=74мм, В30 F300 W6<br>Сетка 5Ср $\frac{100}{100}$ $\frac{100}{100}$ 230хL ГОСТ 23279–85 | м²/м³<br>т | 26,85/1,99<br>0,083 |
| 30 | Устройство покрытия служебного прохода Литой асфальтобетон – 40 мм | м²/м³ | 26,85/1,07 |
| 31 | Устройство штрабы 20х100мм с заполнением резино–битумной мастикой | п.м<br>м³<br>т | 72,20<br>0,15<br>0,27 |
| 32 | Устройство подливки из полимербетона под стойки барьерного ограждения | м³ | 0,10 |
| 33 | Монтаж барьерного ограждения на путепроводе и сопряжении 11МО/Ж(400)–1,1–2,0–0,69 ТУ 5217–055–00110604–2011 | п.м | 52,10 |
| 34 | Монтаж барьерного ограждения на путепроводе и сопряжении 11МО/У7(450)–1,5–2,25–0,98 ТУ 5217–055–00110604–2011 | п.м | 52,10 |
| 35 | Крепление стоек барьерного ограждения<br>Клеевой анкер МКТ V<br>Капсула V–P 24<br>Резьбовая шпилька V–A 24x300<br>Бурение отверстий в железобетоне ø28 , l=210мм | шт.<br><br><br><br>п.м. | 208<br><br><br><br>43,68 |
| 36 | Обработка материалом "жидкое стекло" бетонных поверхностей монолитных цоколей | м² | 108,11 |
| 37 | Устройство перильного ограждения из композитных материалов | п.м./т | 41,65/0,33 |
| 38 | Устройство деформационных швов MAGEBA TENSA GRIP mm RS–LS 100 | п.м | 60,22 |
| 39 | Устройство антиколейных полос ПГМК (BJ BAUM) | п.м | 53,00 |

Примечание

1. Все размеры в мм.
2. Барьерное ограждение принято по ТУ 5217–055–00110604–2011 ЗАО ДЗМК "МЕТАКО".
3. Устройство перехода зоны "ПГМК (BJ BAUM)" осуществлено с дополнительными антиколейными полосами плавного проезда после устройства покрытия проезжей части.
4. При устройстве антиколейных полос "ПГМК (BJ BAUM)", в местах их пересечения с поперечным дренажным каналом, уменьшить толщину заполняемого слоя антиколейных полос до 60мм, в целях сохранения сплошности дренажного канала.
5. Арматурные выпуски ø12 AIII устанавливаются на клеевой эпоксидный состав в предварительно пробуренные отверстия (l.шт=120мм, d=16мм) с шагом 200 мм по всей длине пролетного строения.
6. Для обеспечения отвода конденсата от боковой грани монолитного цоколя БМЦ–1, выравнивающий слой от БМЦ–1 до оси дренажного канала устраивается с уклоном i=0,02 в сторону дренажного канала.
7. Для отвода воды с пролетного строения в монолитной консоли УМК устраиваются "окна" шириной 300мм.
8. Дренажные трубки на тротуаре устраиваются перед бетонированием монолитной консоли УМК.
9. Дренажные трубки на тротуаре устанавливаются с шагом равным шагу дренажных трубок на проезжей части.
10. Крепление водоотводного лотка к пролетному строению осуществляется после бетонирования монолитной консоли УМК.
11. Переходную зону деформационного шва в зоне служебного прохода и между цоколями БМЦ–1 и БМЦС, БМЦ–2 и БМЦС заполнить литым асфальтобетоном.
12. Перед устройством антиколейных полос уточнить ширину полос безопасности. В случае изменения ширины полос безопасности необходимо соответственно изменить расположение в плане антиколейных полос.
13. На всем протяжении монолитных цоколей устраивается доска 20х20 мм, обрезать штрабы постановкой опалубочных элементов, которые после набора прочности бетоном удалить. В штрабах произвести бурение скважин отверстий ø82 мм на глубину 80 мм и ø65 мм на всю толщину плиты под трубки. Установить трубки и воронки. Верх воронки должен быть в уровне низа гидроизоляции. Забести гидроизоляцию в воронку. Установить сетку из стеклоболокна. Установить решетку.
После установки слоя по проекту "Левиит" в штрабы уложить дренирующий материал, приготовленный по рецепту СОЮЗДОРНИИ. В процессе укладки асфальтобетонного покрытия следить за тем, чтобы каналы не покрывали битумной грунтовкой.

Состав дренажной смеси (в порядке закладки в мешалку):
– щебень сухой гравий фракций 5–10мм – 1700–1800 м.ч.
– смола эпоксидная ЗД–20 ГОСТ10587–84* или другая аналогичная – 100 м.ч
– пластификатор – фурфиловый спирт ГОСТ8728–88. (может быть предварительно совмещен со смолой – 8–15 м.ч.
– отвердитель – полиэтиленполиамин ТУ6–02–594–85 – 9–12 м.ч.
или ИТОК.33М – ТУ6–05–186.1–85 – 18–20 м.ч.
Введение большего количества эпоксидной смолы недопустимо.
Приготовленная композиция должна быть уложена в штрабу в течении 40 мин.
Укладывать смесь с легким уплотнением трамбовкой, поверхность загладить.

## 1–1

## Конструкция мостового полотна после ремонта

М 1:75

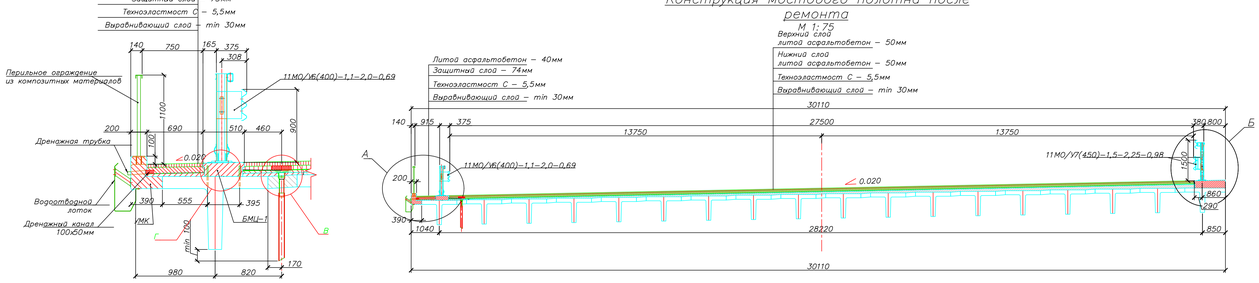


| | | | | | | | |
|---|---|---|---|---|---|---|---|
| | | | | | 82/13–Р–ПИР–34714–КД | | |
| | | | | | Ремонт путепровода через автомобильную дорогу на км 34+714 автомобильной дороги М–2 "Крым" Москва – Тула – Орел – Курск – Белгород – граница с Украиной | | |
| Изм. | Кол.уч. | Лист | № | Подпись | Дата | | |
| ГИП | | Чернобод | | | 07.2013 | Конкурсная документация для проведения подрядных торгов | Стадия П / Лист 3 / Листов |
| Н.контр. | | Чернобод | | | 07.2013 | | |
| Пров. | | Мезенцев | | | 07.2013 | | |
| Разраб. | | Прошкин | | | 07.2013 | Конструкция мостового полотна Начало | Общество с ограниченной ответственностью «Континент» |

Согласовано

Взам. инв. №

Подпись и дата

Инв. № подлинника